
План квартиры по обмеру

0 1 2 м

С размерами · обмер 02.11.2026 · масштаб 1:50 · вход сверху, окна снизу

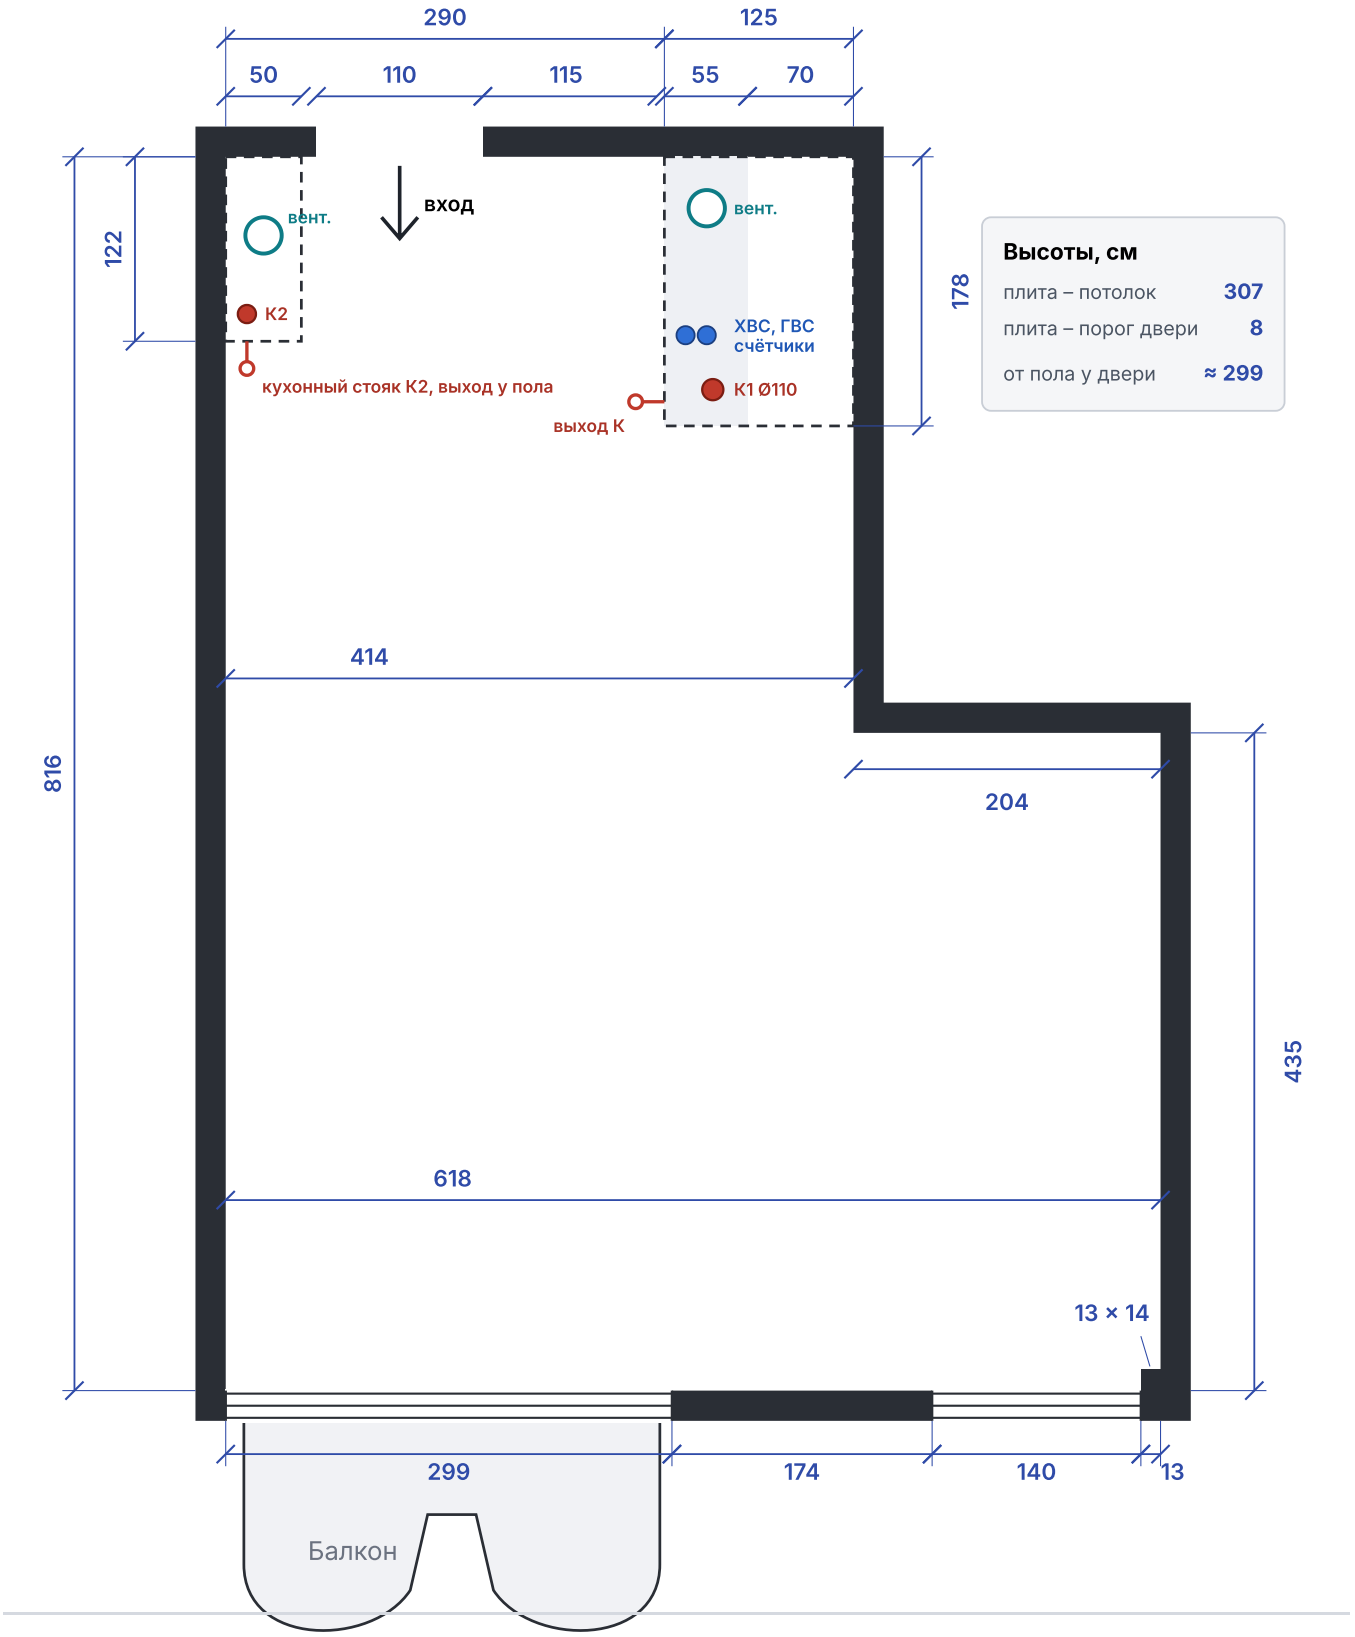

Стены, граница квартиры

Короб – демонтаж

Шахта стояков 55 см

Вентиляция

Водопровод ХВС, ГВС

Канализационные стояки К1, К2

Выход канализации у пола

Окна и дверь на балкон

Размеры – обмер, в сантиметрах, внутренние, до отделки. По окнам 299 + 174 + 140 + 13 = 626 при ширине 618: 8 см расхождения из-за откосов – уточнить; окна и простенок на схеме сжаты пропорционально. Короба шахт демонтируются. Стояки и вентиляция – по фото, ± 10–15 см. Чистовой пол вровень с порогом – до потолка ≈ 299. Печатать на А4 в масштабе 100% – шкала вверху 4 см.